
配料计算实例

作业：计算下图L-1的钢筋配料长度并绘制配料单

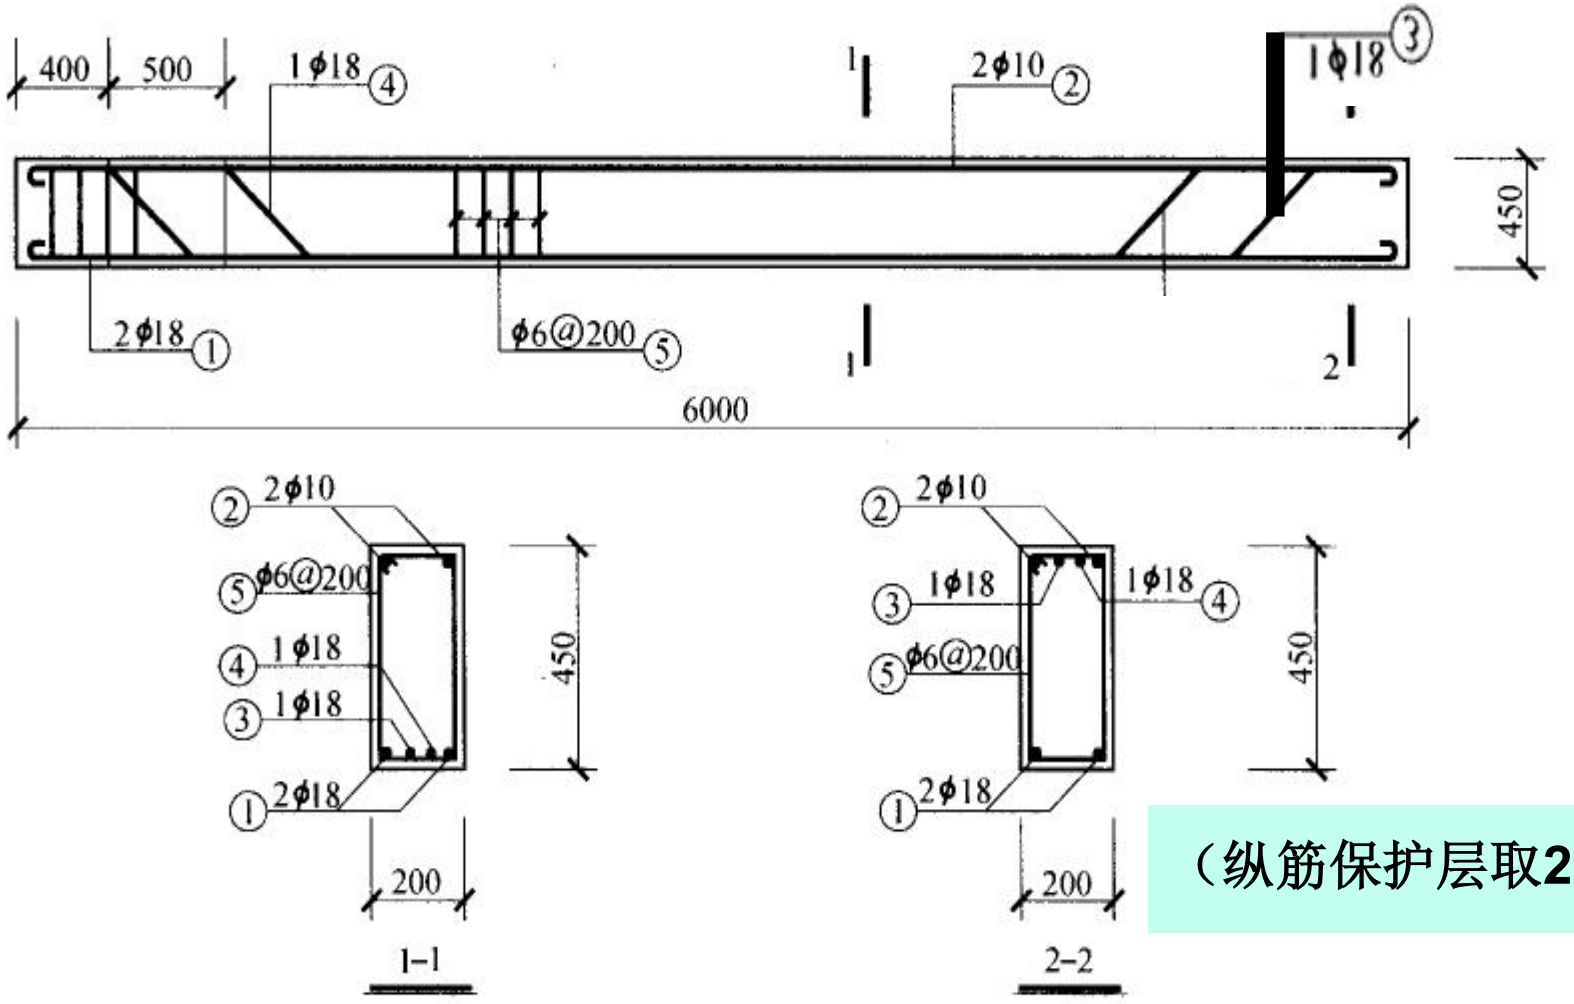

（纵筋保护层取25mm)

图 4-25　L_1 梁钢筋图

配料实例计算结果（纵筋保护层取25mm)

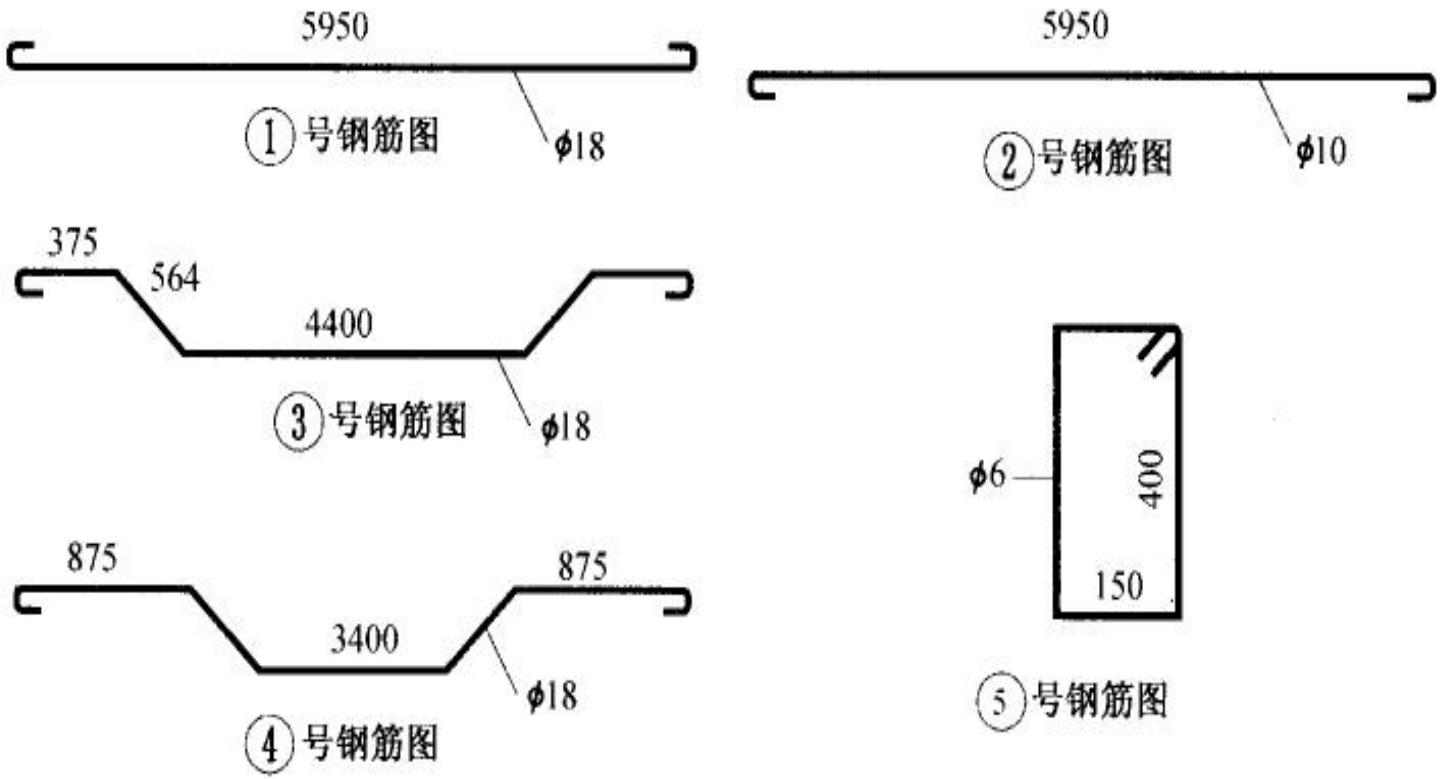


图 4-26 ①~⑤号钢筋图